

МЕЖЕВОЙ ПЛАН	
Общие сведения о кадастровых работах	
1. Межевой план подготовлен в результате выполнения кадастровых работ в связи с:	
образованием земельного участка из земель, находящихся в государственной или муниципальной собственности, расположенного адресу: Российская Федерация, Кемеровская область-КУЗБАСС, муниципальный район Таштагольский, городское поселение Мундыбашское, поселок городского типа Мундыбаш, улица Красноармейская, земельный участок № 1л	
2. Цель кадастровых работ	
3. Сведения о заказчике кадастровых работ:	
Администрация Мундыбашского городского поселения Таштагольского района Кемеровской области-КУЗБАСС	
<i>(фамилия, имя, отчество (при наличии отчества) физического лица, страхового номера индивидуального лицевого счета (при наличии), полное наименование юридического лица, органа государственной власти, органа местного самоуправления, иностранного юридического лица с указанием страны его регистрации (инкорпорации))</i>	
4. Сведения о кадастровом инженере:	
Фамилия, имя, отчество (при наличии отчества):	Бойко Мария Алексеевна
Страховой номер индивидуального лицевого счета:	129-203-766 50
Уникальный регистрационный номер члена саморегулируемой организации кадастровых инженеров в реестре членов саморегулируемой организации кадастровых инженеров и дата внесения сведений о физическом лице в такой реестр:	2409 от 10.11.2016 г.
Контактный телефон:	+79081340755
Почтовый адрес и адрес электронной почты, по которым осуществляется связь с кадастровым инженером: Воронежская область, город Воронеж, улица Ломоносова, д 114/20, кв 74 mari-bespalova@inbox.ru	
Наименование саморегулируемой организации кадастровых инженеров, членом которой является кадастровый инженер: А СРО ОПКД	
Полное или (в случае, если имеется) сокращенное наименование юридического лица, если кадастровый инженер является работником юридического лица, адрес юридического лица: ООО НПП "АЦЛПИ", 187342, Воронежская область, город Воронеж, Жилой массив Олимпийский, д 12, кв 355	

Наименование, номер и дата документа, на основании которого выполняются кадастровые работы: №0139300007521000026_120059 2021-03-29

Дата подготовки межевого плана (число, месяц, год): 11 июня 2021 г.

Исходные данные							
1. Перечень документов, использованных при подготовке межевого плана							
№ п/п	Наименование документа				Реквизиты документа		
1	2				3		
1	Выписка координат из каталога геодезических пунктов в МСК-42				№111/4768, выдан 06.04.2021		
2	Кадастровый план территории				№99/2021/385053967, выдан 02.04.2021		
3	Распоряжение администрации "Об утверждении схемы расположения земельного участка"				№100-р, выдан 06.05.2021		
4	Схема расположения земельных участков на кадастровых планах или кадастровых картах соответствующих территорий				№100-р, выдан 06.05.2021		
5	Распоряжение администрации о присвоении адреса земельному участку				№76-р, выдан 13.04.2021		
6	Распоряжение "О внесении изменений" в Распоряжение "О присвоении адреса земельному участку"				№98-р, выдан 06.05.2021		
7	Выписка ГАР из ФИАС				№FV-210528-735684, выдан 28.05.2021		
2. Сведения о геодезической основе, использованной при подготовке межевого плана							
Система координат МСК-42, зона 2							
№ п/п	Название пункта и тип знака геодезической сети	Класс геодезической сети	Координаты, м		Сведения о состоянии на 22 апреля 2021 г.		
			X	Y	наружног о знака	центра пункта	марки
1	2	3	4	5	6	7	8
1	Жасменка	3 класс	388409,28	2221109,72	сохранился	сохранился	сохранилась

2	Мундыбаш Нов.	3 класс	384150,52	2220974,8 0	сохранил я	сохранил я	сохранила сь
3	Одрабаш	3 класс	386168,20	2227687,3 9	сохранил я	сохранил я	сохранила сь

3. Сведения о средствах измерений

№ п/п	Наименование прибора (инструмента, аппаратуры)	Сведения об утверждении типа средств измерений	Реквизиты свидетельства о поверке прибора (инструмента, аппаратуры)
1	2	3	4
1	Аппаратура геодезическая спутниковая EFT M4 GNSS	75294-19	С-ГСХ/19-03-2021/46004276

4. Сведения о наличии зданий, сооружений, объектов незавершенного строительства на исходных земельных участках

№ п/п	Кадастровый номер земельного участка	Кадастровые или иные номера зданий, сооружений, объектов незавершенного строительства, расположенных на земельном участке
1	2	3
-	-	-

5. Сведения о частях исходных или уточняемых земельных участков

№ п/п	Кадастровый номер земельного участка	Учетные номера частей земельного участка
1	2	3
-	-	-

Сведения о выполненных измерениях и расчетах				
1. Метод определения координат характерных точек границ земельных участков и их частей				
№ п/п	Кадастровый номер или обозначение земельного участка, частей земельного участка	Метод определения координат		
1	2	3		
1	:3У1	Метод спутниковых геодезических измерений (определений) (для точек: 1-27)		
2. Точность положения характерных точек границ земельных участков				
№ п/п	Кадастровый номер или обозначение земельного участка	Формулы, примененные для расчета средней квадратической погрешности положения характерных точек границ (Mt), м		
1	2	3		
1	:3У1	$Mt = \sqrt{(m_0^2 + m_1^2)} = \sqrt{(0.04^2 + 0.09^2)} = 0.1$ (для точек: 1-27)		
3. Точность положения характерных точек границ частей земельных участков				
№ п/п	Кадастровый номер или обозначение земельного участка	Учетный номер или обозначение части	Формулы, примененные для расчета средней квадратической погрешности положения характерных точек границ (Mt), м	
1	2	3	4	
-	-	-	-	
4. Точность определения площади земельных участков				
№ п/п	Кадастровый номер или обозначение земельного участка	Площадь (P), м2	Формулы, примененные для расчета предельной допустимой погрешности определения площади земельного участка (dP), м2	
1	2	3	4	
1	:3У1	337326	$\Delta P = 3,5 * Mt * \sqrt{P}$ док $\Delta P = 3,5 * 0,1 * \sqrt{337326} = 203$	
5. Точность определения площади частей земельных участков				
№ п/п	Кадастровый номер или обозначение земельного участка	Учетный номер или обозначение части	Площадь (P), м2	Формулы, примененные для расчета предельной допустимой погрешности определения площади части земельного участка (dP), м2
1	2	3	4	5
-	-	-	-	-

Сведения об образуемых земельных участках и их частях				
1. Сведения о характерных точках границ образуемых земельных участков				
Обозначение земельного участка: :ЗУ1				
Обозначение характерных точек границ	Координаты, м		Средняя квадратическая погрешность определения координат характерных точек	Описание закрепления точки
	X	Y		
1	2	3	4	5
<i>н1</i>	<i>385954,95</i>	<i>2222184,66</i>	<i>0,10</i>	-
<i>н2</i>	<i>385910,55</i>	<i>2222617,58</i>	<i>0,10</i>	-
<i>н3</i>	<i>385992,65</i>	<i>2222829,39</i>	<i>0,10</i>	-
<i>н4</i>	<i>385973,68</i>	<i>2222835,56</i>	<i>0,10</i>	-
<i>н5</i>	<i>385971,06</i>	<i>2222886,44</i>	<i>0,10</i>	-
<i>н6</i>	<i>386013,97</i>	<i>2223006,54</i>	<i>0,10</i>	-
<i>н7</i>	<i>386032,91</i>	<i>2223005,44</i>	<i>0,10</i>	-
<i>н8</i>	<i>386060,27</i>	<i>2223003,85</i>	<i>0,10</i>	-
<i>н9</i>	<i>386069,13</i>	<i>2223026,71</i>	<i>0,10</i>	-
<i>н10</i>	<i>385946,65</i>	<i>2223025,02</i>	<i>0,10</i>	-

<i>н11</i>	<i>385609,25</i>	<i>2223020,37</i>	<i>0,10</i>	-
<i>н12</i>	<i>385590,22</i>	<i>2222747,61</i>	<i>0,10</i>	-
<i>н13</i>	<i>385714,11</i>	<i>2222807,46</i>	<i>0,10</i>	-
<i>н14</i>	<i>385723,20</i>	<i>2222779,55</i>	<i>0,10</i>	-
<i>н15</i>	<i>385720,33</i>	<i>2222753,76</i>	<i>0,10</i>	-
<i>н16</i>	<i>385728,97</i>	<i>2222733,41</i>	<i>0,10</i>	-
<i>н17</i>	<i>385737,22</i>	<i>2222713,00</i>	<i>0,10</i>	-
<i>н18</i>	<i>385733,51</i>	<i>2222706,31</i>	<i>0,10</i>	-
<i>н19</i>	<i>385705,39</i>	<i>2222690,62</i>	<i>0,10</i>	-
<i>н20</i>	<i>385694,21</i>	<i>2222659,29</i>	<i>0,10</i>	-
<i>н21</i>	<i>385694,11</i>	<i>2222650,15</i>	<i>0,10</i>	-
<i>н22</i>	<i>385693,92</i>	<i>2222631,34</i>	<i>0,10</i>	-
<i>н23</i>	<i>385694,38</i>	<i>2222619,15</i>	<i>0,10</i>	-
<i>н24</i>	<i>385695,03</i>	<i>2222601,52</i>	<i>0,10</i>	-

<i>н25</i>	<i>385647,31</i>	<i>2222560,49</i>	<i>0,10</i>	-
<i>н26</i>	<i>385466,53</i>	<i>2222038,77</i>	<i>0,10</i>	-
<i>н27</i>	<i>385820,16</i>	<i>2222035,60</i>	<i>0,10</i>	-
<i>н1</i>	<i>385954,95</i>	<i>2222184,66</i>	<i>0,10</i>	-
-	-	-	-	-

2. Сведения о частях границ образуемых земельных участков

Обозначение земельного участка: :ЗУ1

Обозначение части границ		Горизонтальное проложение (S), м	Описание прохождения части границ
от т.	до т.		
1	2	3	4
<i>н1</i>	<i>н2</i>	<i>435,19</i>	-
<i>н2</i>	<i>н3</i>	<i>227,16</i>	-
<i>н3</i>	<i>н4</i>	<i>19,95</i>	-
<i>н4</i>	<i>н5</i>	<i>50,95</i>	-
<i>н5</i>	<i>н6</i>	<i>127,54</i>	-
<i>н6</i>	<i>н7</i>	<i>18,97</i>	-
<i>н7</i>	<i>н8</i>	<i>27,41</i>	-
<i>н8</i>	<i>н9</i>	<i>24,52</i>	-
<i>н9</i>	<i>н10</i>	<i>122,49</i>	-
<i>н10</i>	<i>н11</i>	<i>337,43</i>	-
<i>н11</i>	<i>н12</i>	<i>273,42</i>	-
<i>н12</i>	<i>н13</i>	<i>137,59</i>	-
<i>н13</i>	<i>н14</i>	<i>29,35</i>	-
<i>н14</i>	<i>н15</i>	<i>25,95</i>	-
<i>н15</i>	<i>н16</i>	<i>22,11</i>	-
<i>н16</i>	<i>н17</i>	<i>22,01</i>	-
<i>н17</i>	<i>н18</i>	<i>7,65</i>	-
<i>н18</i>	<i>н19</i>	<i>32,2</i>	-
<i>н19</i>	<i>н20</i>	<i>33,27</i>	-
<i>н20</i>	<i>н21</i>	<i>9,14</i>	-
<i>н21</i>	<i>н22</i>	<i>18,81</i>	-
<i>н22</i>	<i>н23</i>	<i>12,2</i>	-
<i>н23</i>	<i>н24</i>	<i>17,64</i>	-
<i>н24</i>	<i>н25</i>	<i>62,93</i>	-
<i>н25</i>	<i>н26</i>	<i>552,15</i>	-
<i>н26</i>	<i>н27</i>	<i>353,64</i>	-

н27	н1	200,97	-	
3. Сведения о местоположении границ частей образуемых земельных участков				
Обозначение земельного участка: -				
Учетный номер или обозначение части: -				
Обозначение характерных точек границ	Координаты, м		Средняя квадратическая погрешность определения координат характерных точек	Описание закрепления точки
	X	Y		
1	2	3	4	5
-	-	-	-	-
3.1. Сведения об образовании земельных участков путем перераспределения				
Обозначение земельного участка: -				
№ п/п	Источник образования		Сведения о частях земельных участков (территориях) включаемых в состав образуемого земельного участка	
	Кадастровый номер земельного участка (учетный номер кадастрового	Площадь (Р),	Обозначение	Площадь (Р),
1.0	2	3	4	5
-	-	-	-	-

4. Общие сведения об образуемых земельных участках

Обозначение земельного участка: :ЗУ1

№ п/п	Наименование характеристик земельного участка	Значение характеристики
1	2	3
1	Адрес земельного участка или описание его местоположения	Российская Федерация, Кемеровская область-КУЗБАСС, муниципальный район Таштагольский, городское поселение Мундыбашское, поселок городского типа Мундыбаш, улица Красноармейская, земельный участок 1л
2	Местоположение земельного участка в структурированном виде в соответствии с федеральной информационной адресной системой (при отсутствии адреса земельного участка)	
3	Категория земель	Земли населенных пунктов
4	Вид разрешенного использования	охрана природных территорий
5	Площадь земельного участка величина погрешности определения площади ,	337326 ± 203
6	Предельный минимальный и максимальный размер земельного участка (Рмин) и (Рмакс),	100 -
7	Кадастровый или иной номер здания, сооружения, объекта незавершенного строительства, расположенного на земельном	-
8	Условный номер земельного участка	-
	Учетный номер проекта межевания территории	-
	Реестровый номер границ	42:12- 6.857, 42:12-6.858
9	Иные сведения	-

5. Общие сведения о частях образуемых земельных участков

Обозначение земельного участка: :ЗУ1

№ п/п	Учетный номер или обозначение части	Площадь (Р), м²	±ΔР, м²	Характеристика части
1	2	3	4	5
Обозначение земельного участка: -				
№ п/п	Учетный номер или обозначение части	Площадь (Р), м²	±ΔР, м²	Характеристика части
1	2	3	4	5

-	-	-	-	-
---	---	---	---	---

6. Сведения о земельных участках, смежных с образуемым земельным участком с обозначением :ЗУ1

Обозначение характерной точки или части границ	Кадастровые номера земельных участков, смежных с образуемым земельным участком	Сведения о правообладателях смежных земельных участков
1	2	3

7. Сведения об обеспечении доступа (прохода или проезда от земель общего пользования, земельных участков общего пользования, территории общего пользования) к образуемым или измененным земельным участкам

№ п/п	Кадастровый номер или обозначение земельного участка, для которого обеспечивается доступ	Сведения о земельных участках (землях общего пользования, территории общего пользования), посредством которых обеспечивается доступ
1	2	3

Заключение кадастрового инженера


Межевой план подготовлен в результате проведения кадастровых работ по муниципальному контракту №0139300007521000026_120059 от 29.03.2021 г. в связи с образованием земельного участка площадью 337 326 кв. м. из земель, находящихся в государственной или муниципальной собственности, расположенного по адресу: Российская Федерация, Кемеровская область-КУЗБАСС, муниципальный район Таштагольский, городское поселение Мундыбашское, поселок городского типа Мундыбаш, улица Красноармейская, земельный участок № 1л в кадастровом квартале 42:12:0106002.

На основании Решения Совета народных депутатов Мундыбашского городского поселения от «12» декабря 2016г № 17/1. " Правила землепользования и застройки в Мундыбашском городском поселении"» земельный участок расположен в зоне Ж-2, согласно ПЗЗ минимальный предел размер земельного участка с видом разрешенного использования "охрана природных территорий" - 100 кв.м, а максимальный размер- не установлен, отсюда следует, что земельный участок соответствует Требованиям к ПЗЗ и межевому плану и препятствий для осуществления кадастрового учета нет.

Ссылка на ПЗЗ в сети "Интернет" <https://mundybash.ru/category/gradostroitelstvo/pzz/>

Кадастровый инженер- Бойко Мария Алексеевна (реестровый №-36864). СНИЛС: № 129-203-766 50. Является членом- Ассоциации СРО "Объединение профессионалов кадастровой деятельности", и включен в реестр членов Ассоциации СРО "ОПКД" 10.11.2016 за регистрационным номером № 2409 (№ реестровой записи от 08.07.2016 г. № 003).

Чертеж земельных участков и их частей

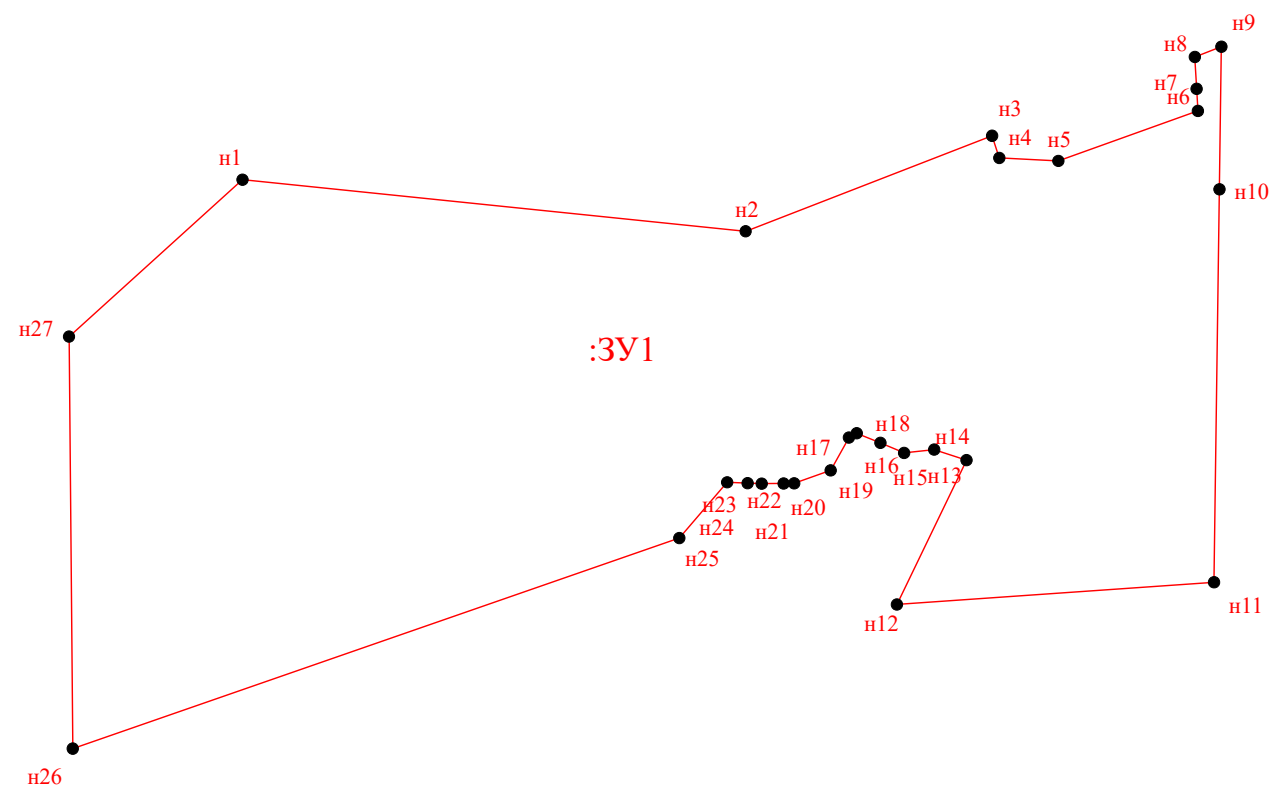

Масштаб 1:6500

Условные обозначения:

- - вновь образованная часть границы, сведения о которой достаточны для определения ее местоположения на местности;
- н4 - характерная точка границы уточняемого земельного участка, установленного при проведении кадастровых работ;
- :3У1 - обозначение образуемого земельного участка

Схема геодезических построений


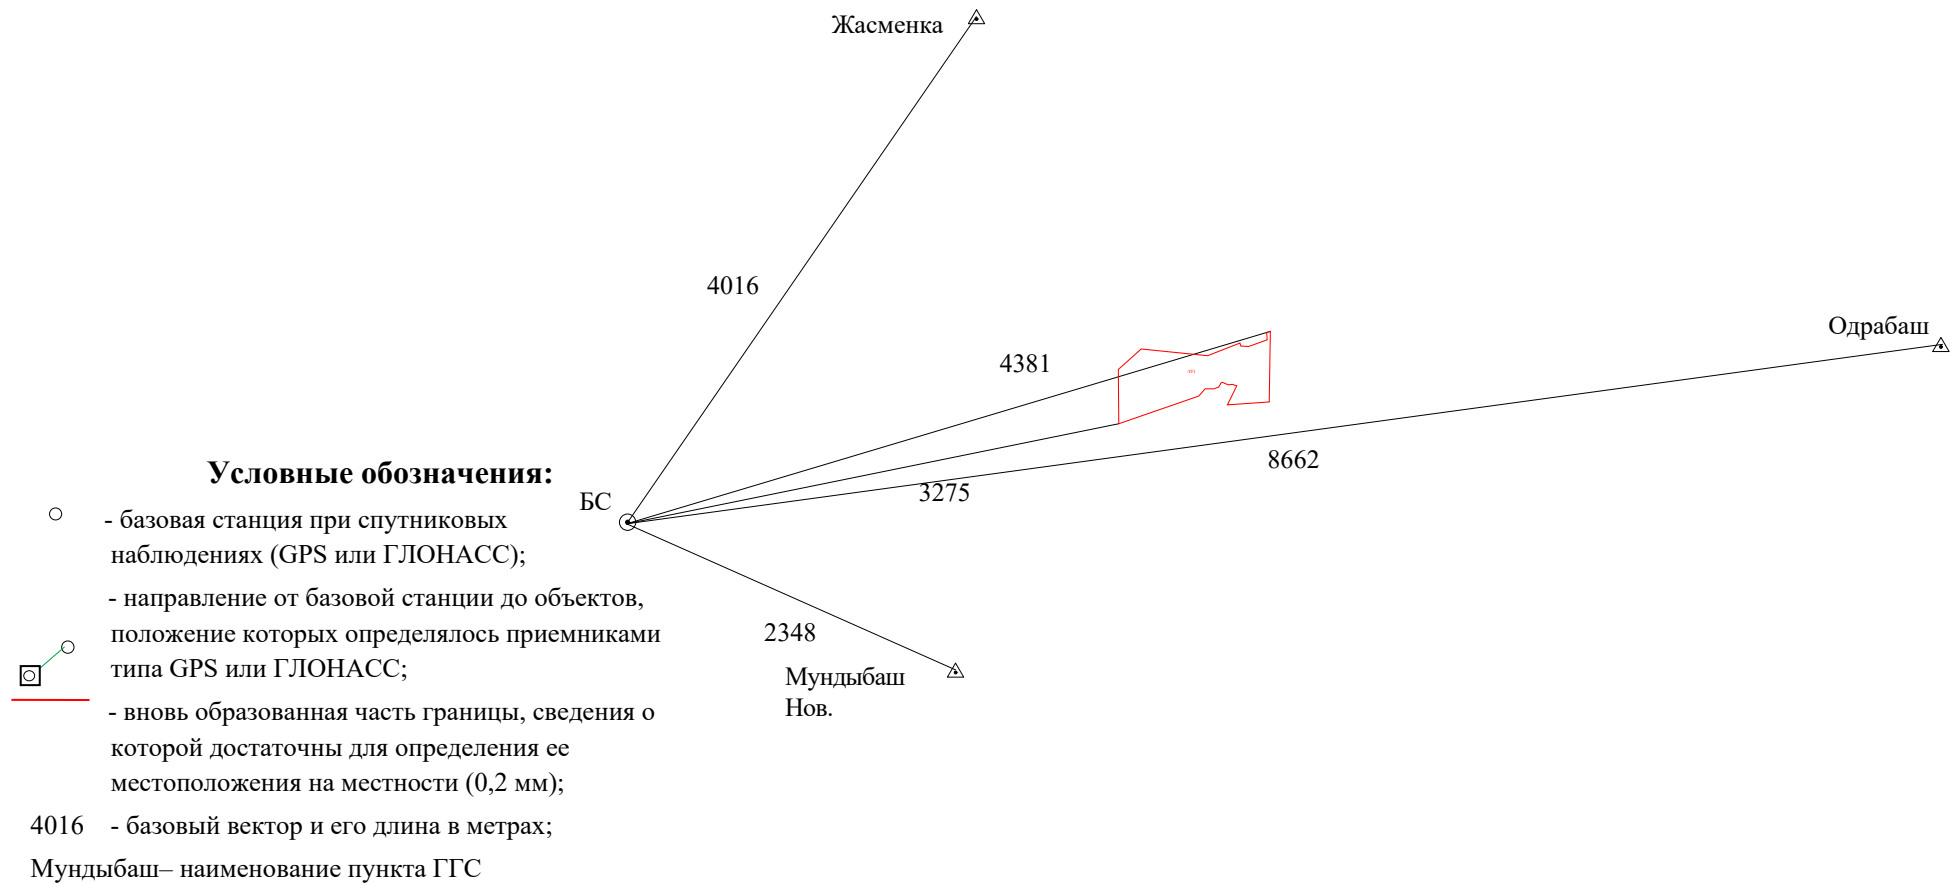


Схема расположения земельных участков и их частей

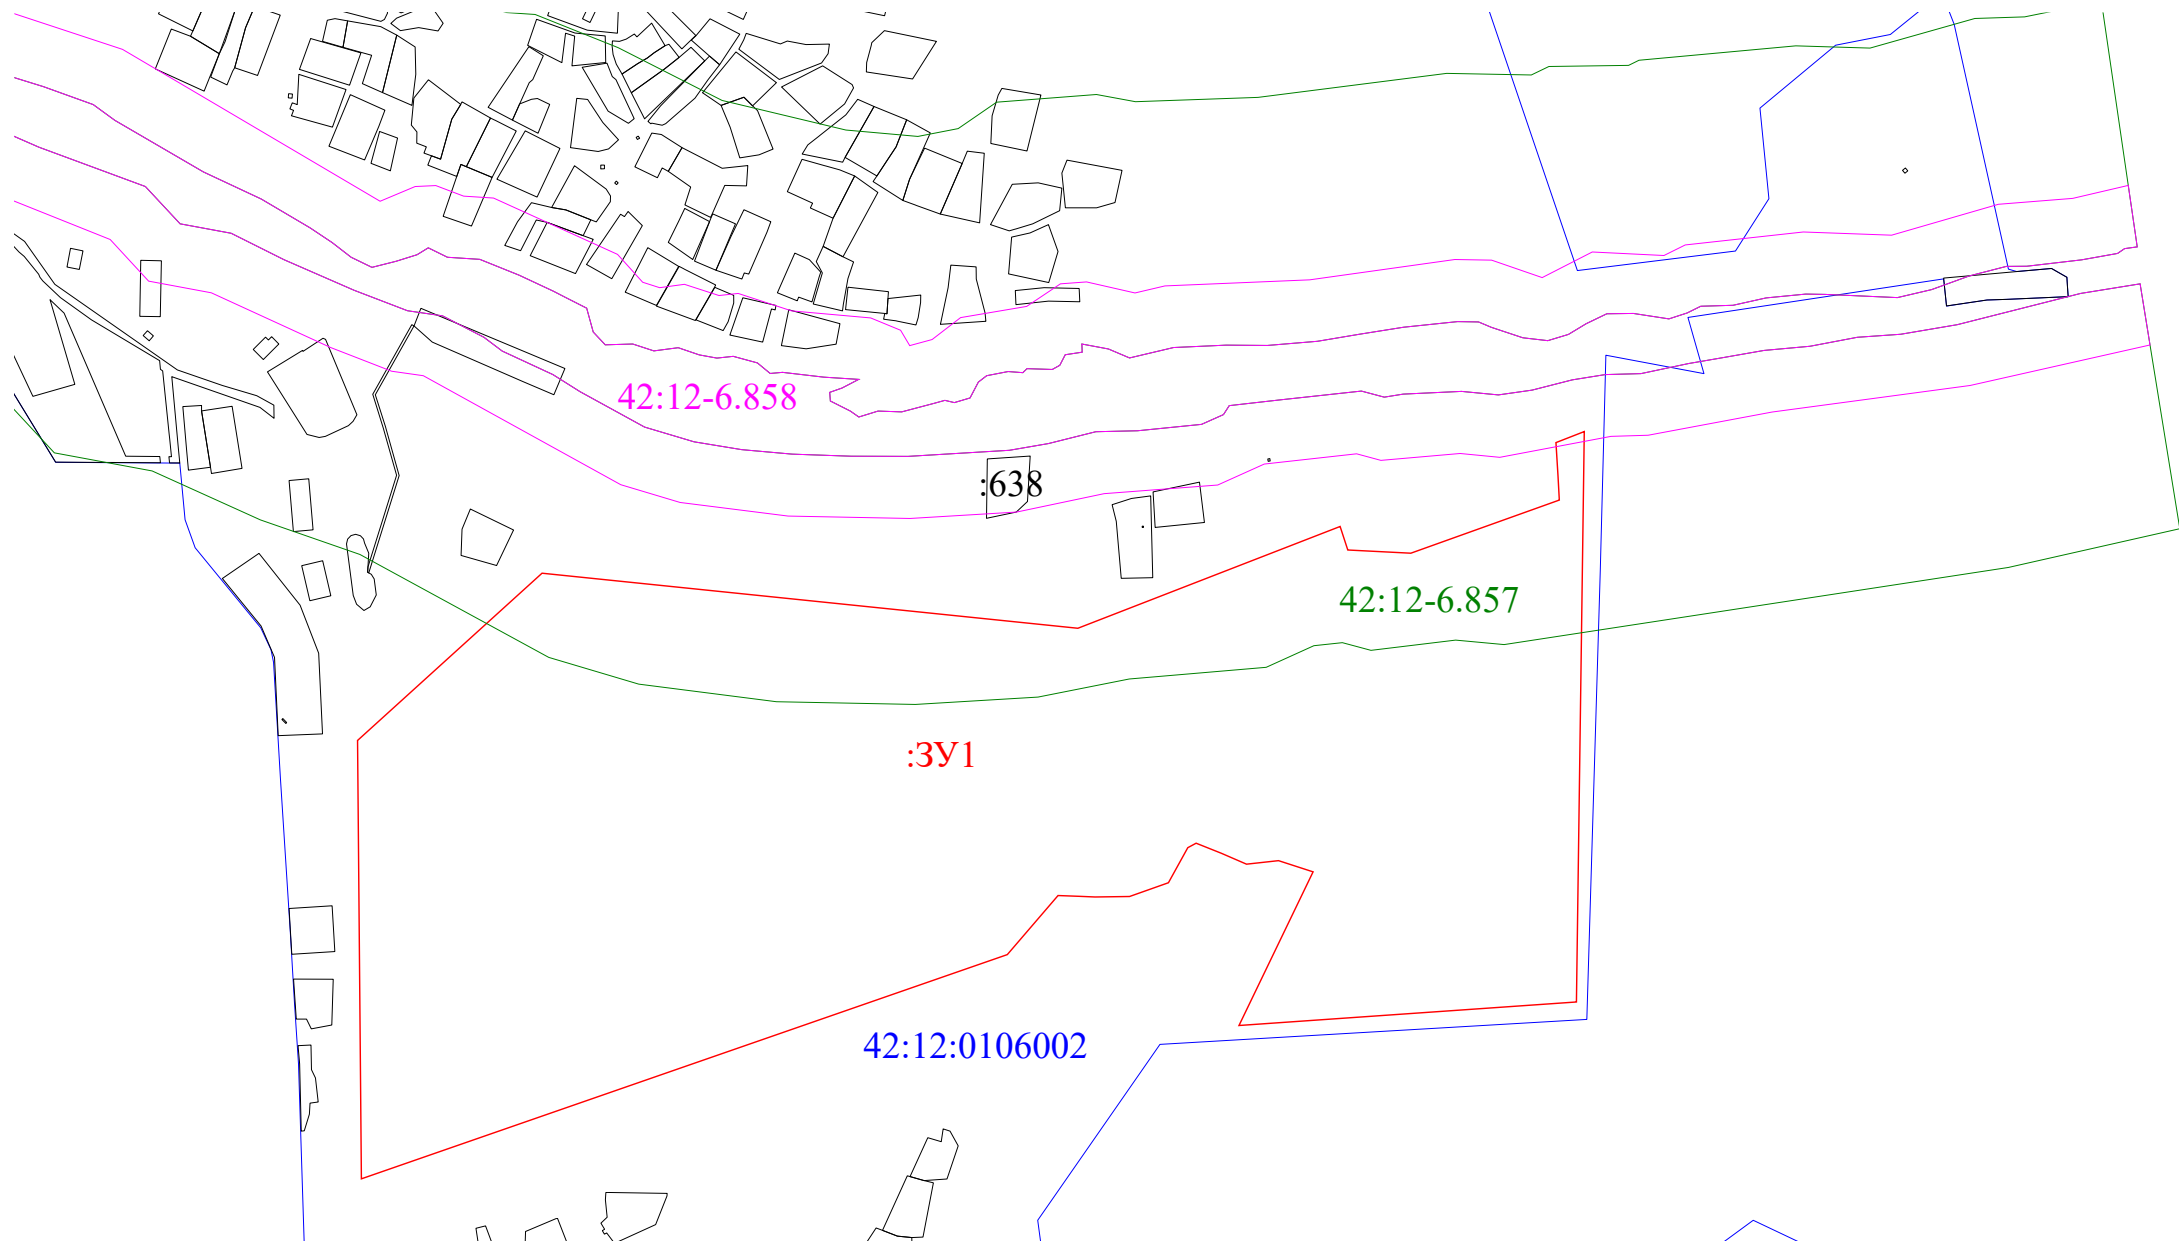

Масштаб 1:5000

- Условные обозначения:**
- - вновь образованная часть границы, сведения о которой достаточны для определения ее местоположения на местности;
 - :3У1 - обозначение образуемого участка;
 - - граница земельного участка, включенного в ЕГРН;
 - - граница кадастрового квартала;
 - :638 - кадастровый номер земельного участка, включенного в ЕГРН,
 - 42:12:0106002 - кадастровый номер квартала
 - 42:12- 6.857- граница зоны с особыми условиями использования территории
 - 42:12-6.858 - граница зоны с особыми условиями использования территории