

Проект индивидуального 1-этажного жилого дома из газобетона
площадью 60 кв м
Архитектурно-строительные решения



Ведомость рабочих чертежей основного комплекта АС

Лист	Наименование	Примечание
4	Общие данные	
5	Общие данные	
6	Общие данные	
7	Планировка	
8	Планировка с расстановкой мебели	
9	Эскиз фасадов 1,3	
10	Эскиз фасадов 2,4	
11	Разрез 1-1	
12	План ростверка	
13	План ростверка со сваями	
14	Схема армирования ростверка	
15	Схема расположения продухов в ростверке	
16	Узлы армирования ростверка	
17	План перекрытия цоколя	
18	Развертка фасадов по каменной кладке 1,2	
19	Развертка фасадов по каменной кладке 3,4	
20	Схема устройства армопояса	
21	Разрез по вентиляционной трубе	
22	План кровли	
23	Схема расположения мауэрлата	
24	Схема раскладки стропил	

						АС			
Изм.	Кол. уч.	Лист	№ док.	Подп.	Дата				
Инж.-арх		Цветкова				одноэтажный дом площадью 60 кв.м.	Стадия	Лист	Листов
							П	2	28

Ведомость рабочих чертежей основного комплекта АС

(Продолжение)

25	Схема раскладки стропил	
26	Узлы кровли	
27	Узлы кровли- вариант для мягкой кровли	
28	Схема металлического крыльца	
29	Узел наружного оконного откоса	

[illegible]

ОБЩИЕ ДАННЫЕ

Объект проектирования располагается в Ивановской области, в зоне со следующими климатическими условиями:

1. Климат умеренно-континентальный, среднегодовая температура воздуха составляет + 4,1°С, абсолютный минимум -45°С, максимум +38 °С.
2. В соответствии с СП 131.13330.2018 климатический район строительства-II-B;
3. Согласно СП 20.13330.2016 «Нагрузки и воздействия» ветровой район- I, где нормативное значение ветрового давления составляет 0,23 кПа; снеговой район- IV, где нормативный вес снегового покрова составляет 2кПа.

Характеристика проектируемого здания:

- класс сооружения: КС-2;
- степень огнестойкости: II;
- класс конструктивной пожарной опасности здания: С1;
- класс функциональной пожарной опасности здания: Ф1.

4. При строительстве в регионах, имеющих другие климатические районы необходимо уточнить пирог утепления теплового контура в соответствии с местными климатическими условиями.

5. Проект разработан в соответствии с действующими нормами, правилами и стандартами. Технические решения, принятые в настоящем проекте, соответствуют требованиям экологических, санитарно-гигиенических, противопожарных и других норм, действующих на территории РФ и обеспечивают безопасную для жизни и здоровья людей эксплуатацию объекта при соблюдении предусмотренных проектом решений.

6. Рабочие чертежи марки АС разработаны на основании объемно-планировочных решений и технического задания на проектирование заказчика, а также на положениях следующих нормативных документов:

- СП 82.13330.2016 "Благоустройство территорий";
- СП 70.13330.2012 "Несущие и ограждающие конструкции";
- СНиП 21-01-97* "Пожарная безопасность зданий и сооружений";
- СП 55.13330.2016 "Дома жилые одноквартирные. Актуализированная редакция СНиП 31-02-2001";
- СП 131.13330.2018 "Строительная климатология";
- СП 427.1325800.2018 "Каменные и армокаменные конструкции";
- СП 339.1325800.2017 "Конструкции из ячеистых бетонов. Правила проектирования";
- СТО 87313302.13330-001-2012 "Конструкции с применением автоклавного газобетона в строительстве зданий и сооружений";
- СП 29.13330.2011 "Полы";
- СП 64.13330.2017 "Деревянные конструкции";
- СП 22.13330.2016 "Основания зданий и сооружений";
- СП 17.13330.2017 "Кровли";
- ГОСТ 530-2012 "Кирпич и камень керамические" и др.

Согласовано

Взам. инв. №

Подпись и дата

Инв. № подл.

АС

Изм.	Кол. уч.	Лист	№ док.	Подп.	Дата				
Инж.-арх		Цветкова				одноэтажный дом площадью 60 кв.м.	Стадия	Лист	Листов
							П	4	28
						Общие данные			

7. Проектируемый объект представляет собой отдельно стоящий одноэтажный жилой дом с габаритными размерами-10,8х6,8м (по несущим стенам).

Пространственно-планировочная организация индивидуального жилого дома определена его функциональным назначением. Планировочное решение выполнено по заданию заказчика в соответствии с СП 55.13330.2016.

При формировании помещений, как первичных структурных элементов, были учтены пространственные зоны таких бытовых процессов как сон, отдых, приготовление/прием пищи, личная гигиена/туалет, а так же зоны размещения и обслуживания инженерных коммуникаций.

В проекте предусмотрены следующие помещения:

- холл;
- кухня;
- гостиная;
- кладовая;
- санузел;
- тамбур;
- 2 спальни.

8. За условную отметку 0,000 принята отметка верха пола 1 этажа, соответствующая абсолютной отметке.

Наружные стены толщиной 400 мм выполнены из стеновых газобетонных блоков 600х200х400 мм плотностью D400 и отделочным слоем из декоративной облицовочной штукатурки (Ceresit Atlantic-1), внутренние несущие стены толщиной 400 мм выполнены также из газобетонных блоков 600х200х400 мм плотностью D400. По всей площади дома утепление крыши производится по скату кровли. Покрытие кровли – металлочерепица RAL7024. (Возможна замена на мягкую кровлю Технониколь Кантри Мичеган) Перегородки – 200 мм из газобетонных блоков 600х200х400 мм плотностью D400. Окна и двери в наружных стенах с ламинацией – ПВХ по индивидуальному заказу.

9. По периметру наружных стен здания необходимо выполнить бетонную отмостку шириной 1,2 м с уклоном от здания по щебеночному основанию. (либо с покрытием тротуарной плиткой).

10. Рабочая документация разработана для производства работ в летнее время.

11. Указания для производства работ в зимних условиях:

- при производстве работ нулевого цикла необходимо предусмотреть мероприятия, исключающие предзимнее увлажнение грунта основания;
- бетонирование монолитных фундаментов и армопоясов в зимних условиях производить с электроподогревом;
- выполнять своевременное утепление фундаментов – разработать проект производства работ согласно СНиП 3.03.01-87 "Несущие и ограждающие конструкции".
- СП 22.13330.2016 "Основания зданий и сооружений.;
- СП 17.13330.2017 "Кровли";
- ГОСТ 530-2012 "Кирпич и камень керамические" и др.

Согласовано

Взам. инв. №

Подпись и дата

Инв. № подл.

АС

Изм.	Кол.уч.	Лист	№ док.	Подп.	Дата
Инж.-арх		Цветкова			

АС			
одноэтажный дом площадью 60 кв.м.		Стадия	Лист
		П	5
Общие данные		Листов	
		28	


12. Не выполнять работы по покраске фасадов в зимнее время.
13. При устройстве монолитных фундаментов и монолитных участков опалубка должна соответствовать ГОСТ Р 52085-2003.
14. Земляные работы, основания и фундаменты выполнять согласно требованиям СНиП 3.02.01-87 "Земляные сооружения, основания и фундаменты", СП 50-101-2004 "Проектирование и устройство оснований и фундаментов зданий и сооружений".
15. При производстве строительно-монтажных работ руководствоваться требованиями :
 -СНиП 12-01-2004 "Организация строительства."
 -СНиП 3.02.01-87 "Земляные сооружения, основания и фундаменты."
 -СНиП 3.03.01-87 "Несущие и ограждающие конструкции."
 -СНиП 3.04.03-85 "Защита строительных конструкций и сооружений от коррозии."
 -СНиП 12-03-2001 "Безопасность труда в строительстве. Часть 1. Общие требования".
 -СНиП 12-04-2002 "Безопасность труда в строительстве. Часть 2. Строительное производство".
16. Деревянные элементы стропил обработать раствором антисептика и антипирена в соответствии с указаниями СНиП II-25-80 "Деревянные конструкции", ГОСТ 28815-96, ТУ 400-1-185-79.
17. Поверхности всех деревянных элементов обработать составом Барьер-ОБ ТУ 2140-001-772000949276-2001.
18. Деревянные конструкции, соприкасающиеся с каменными конструкциями защитить от гниения прокладкой из двух слоев гидроизоляции.
19. Металлические элементы покрасить пентафталевой эмалью за два раза ПФ- 115 ГОСТ 6465-76 по одному слою грунта ГФ-021 ГОСТ 25129-82.
20. Стропила, кобылки и обрешетку выполнить из древесины хвойных пород по ГОСТ 9463-88 влажностью не более 25%.
21. Стыки элементов обрешетки выполнять на стропильных ногах.
22. В случае неустойчивости стропильной конструкции кровли после подшивки карнизных полок и обрешетки - ее расшатывание - выполнить диски жесткости в вертикальной и горизонтальной плоскости.
23. Все стропильные ноги, затяжки, стойки, кобылки и лобовые доски выполнить сечением 25х100, 50х50, 50х150 и 50х200 мм.
24. Контробрешетку выполнить сечением 50х50 мм.
25. Обрешетку выполнить сечением 25х100 мм.
26. Утепление кровли принять из мин. утеплителя толщиной 200-250 мм.

Согласовано

Взам. инв. №							
	Подпись и дата						
Инв. № подл.							

АС									
Изм.	Кол. уч.	Лист	№ док.	Подп.	Дата				
Инж.-арх		Цветкова							
одноэтажный дом площадью 60 кв.м.						Стадия	Лист	Листов	
						П	6	28	
Общие данные									

Планировка дома из газобетона площадью 60 м2

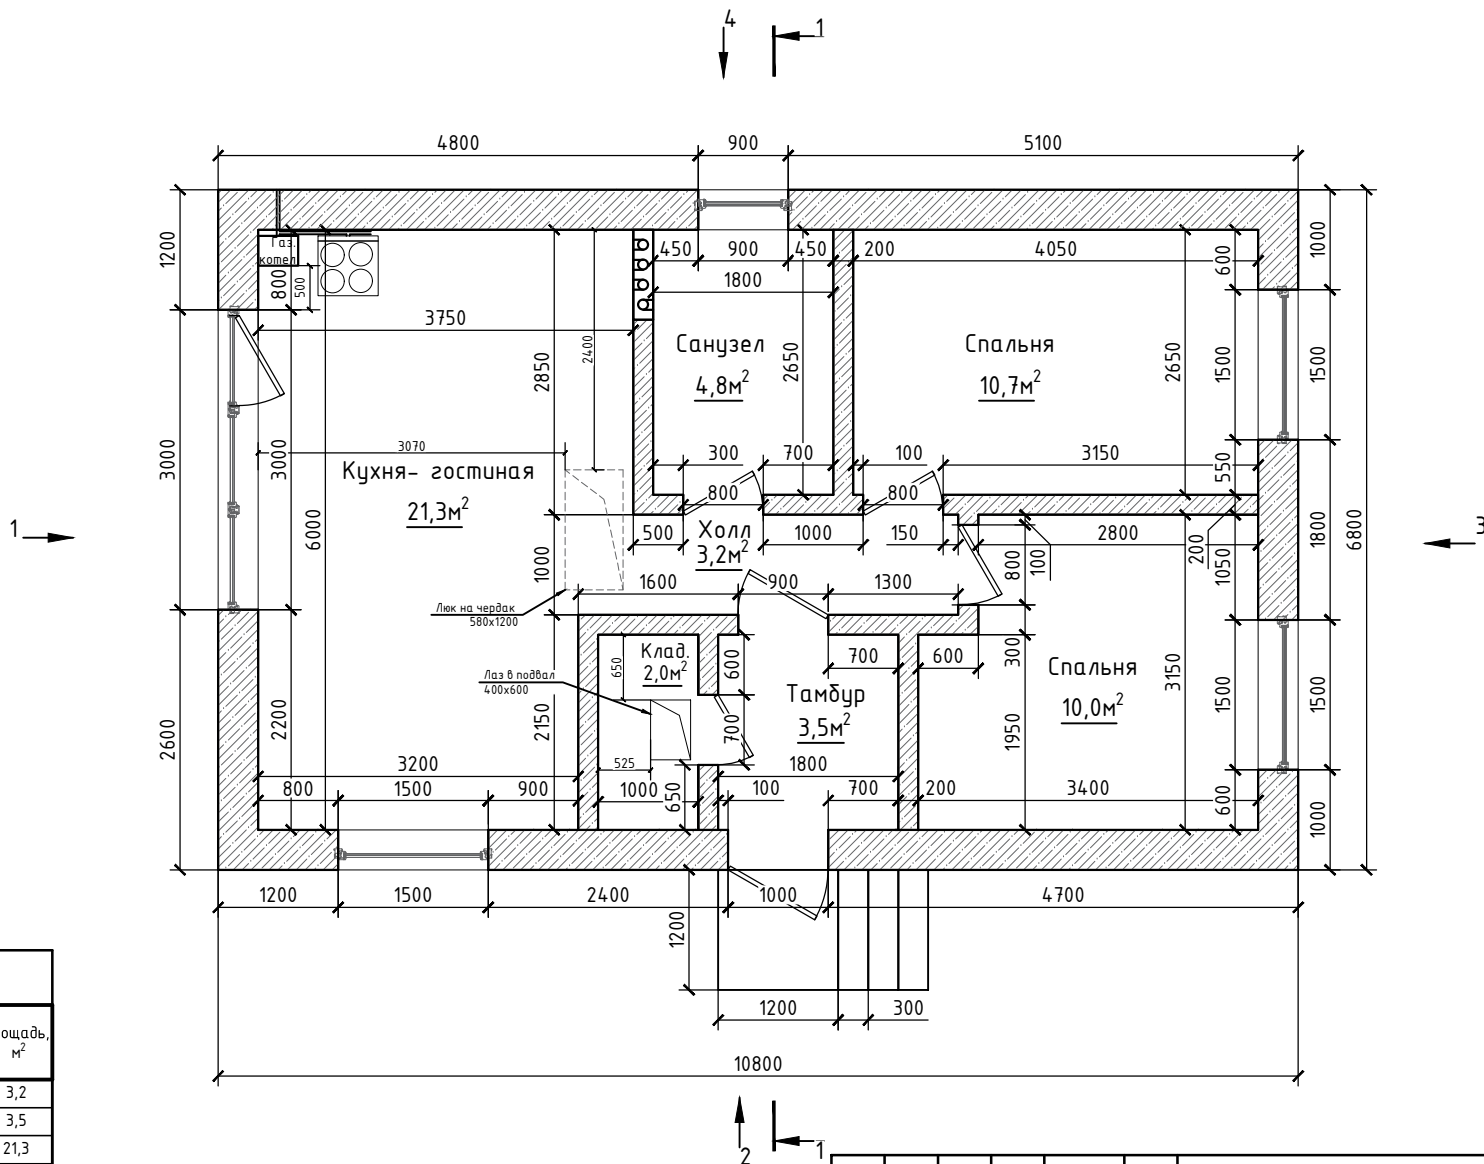


Экспликация помещений		
Номер помеще-ния	Наименование	Площадь, м²
1	Холл	3,2
2	Тамбур	3,5
3	Кухня- гостиная	21,3
4	Спальня	10,7
5	Спальня	10,0
6	Санузел	4,8
7	Кладовая	2,0

Примечания:
1) Площадь дома измеряется по внутреннему контуру наружных несущих стен
2) Для всех необозначенных проёмов принять высоту 2080 мм от ч.п. или 2220 мм от верха плиты перекрытия

						АС			
Изм.	Кол.ч	Лист	№ док.	Подп.	Дата				
Инж.-арх		Цветкова				одноэтажный дом площадью 60 кв.м.	Стация	Лист	Листов
							П	7	28
						Архитектурно-строительные решения			

Планировка с расстановкой мебели

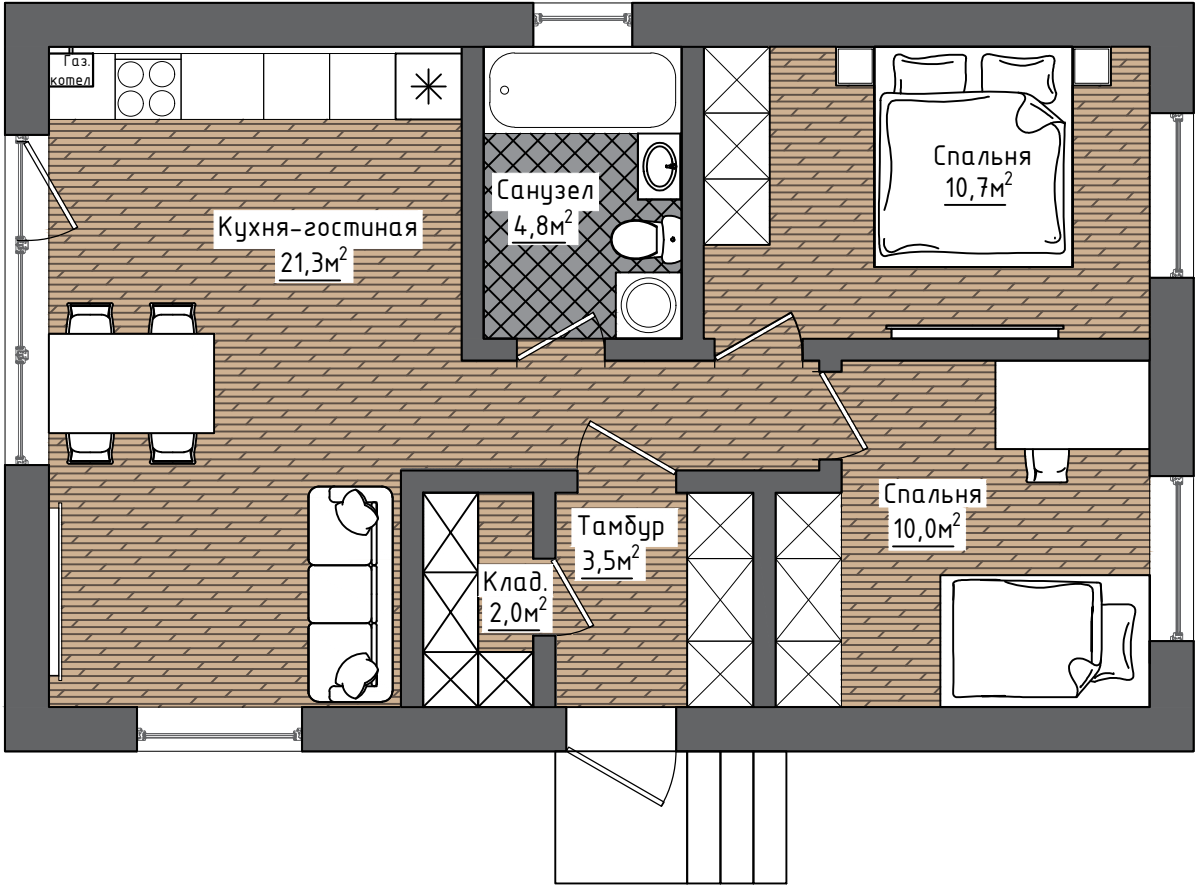


Примечания:

- 1) Соблюсти отступ от окон до газового оборудования – не менее 500 мм
- 2) Тамбур не является обязательным


						АС		
Изм.	Кол.ч	Лист	№ док.	Подп.	Дата	одноэтажный дом площадью 60 кв.м.	Стадия	Лист
Инж.-арх	Цветкова						П	8
						Архитектурно-строительные решения		28

Эскиз фасадов 1,3

1

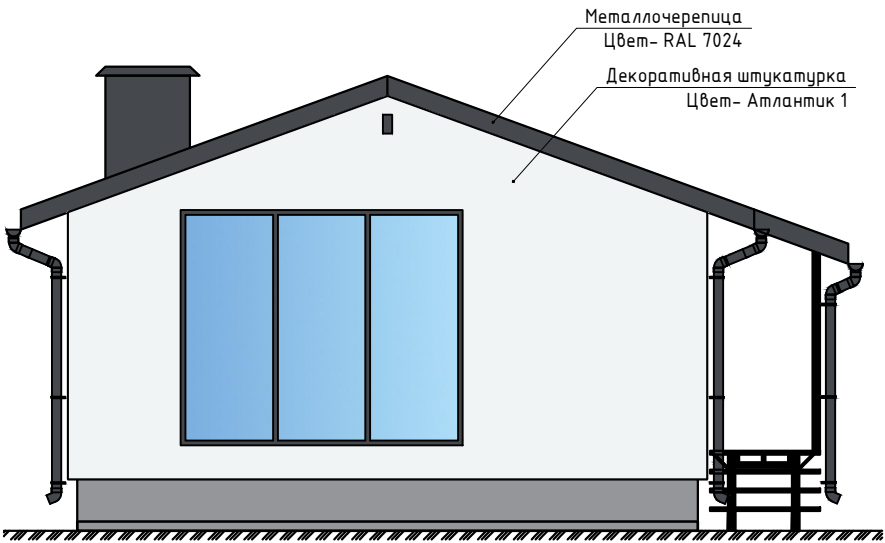

3

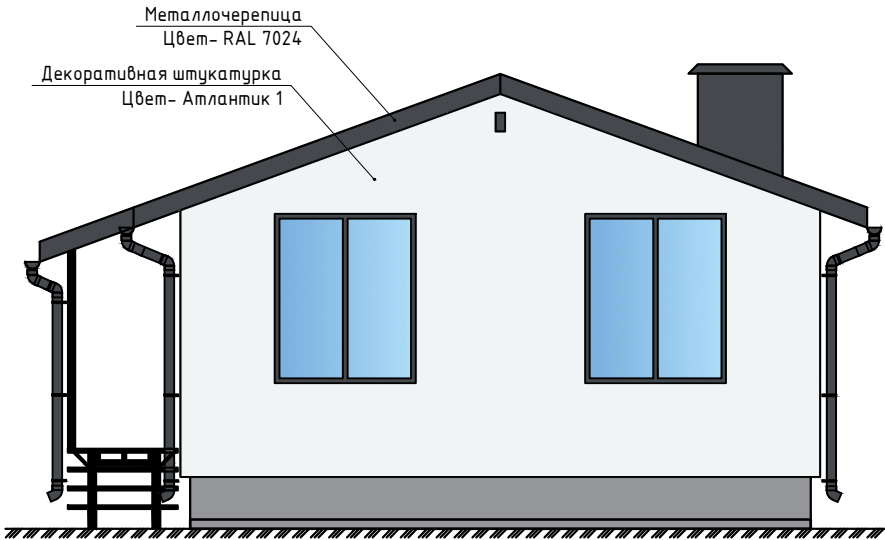


Количество и конфигурация секций в окнах показаны условно и уточняются на этапе согласования окон с производителем


Согласовано						
Взам. инв. №						
Подпись и дата						
Инв. № подл.						

						АС					
Изм.	Кол.уч.	Лист	№ док.	Подп.	Дата						
Инж.-арх	Цветкова					одноэтажный дом площадью 60 кв.м.			Стадия	Лист	Листов
									П	9	28
						Архитектурно-строительные решения					

2

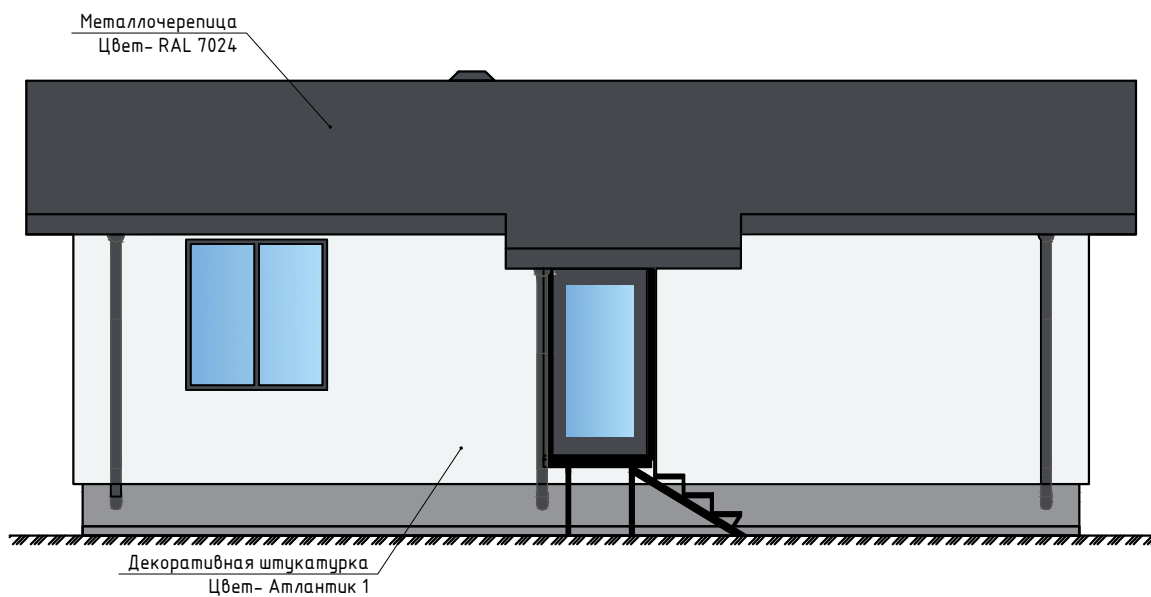


4

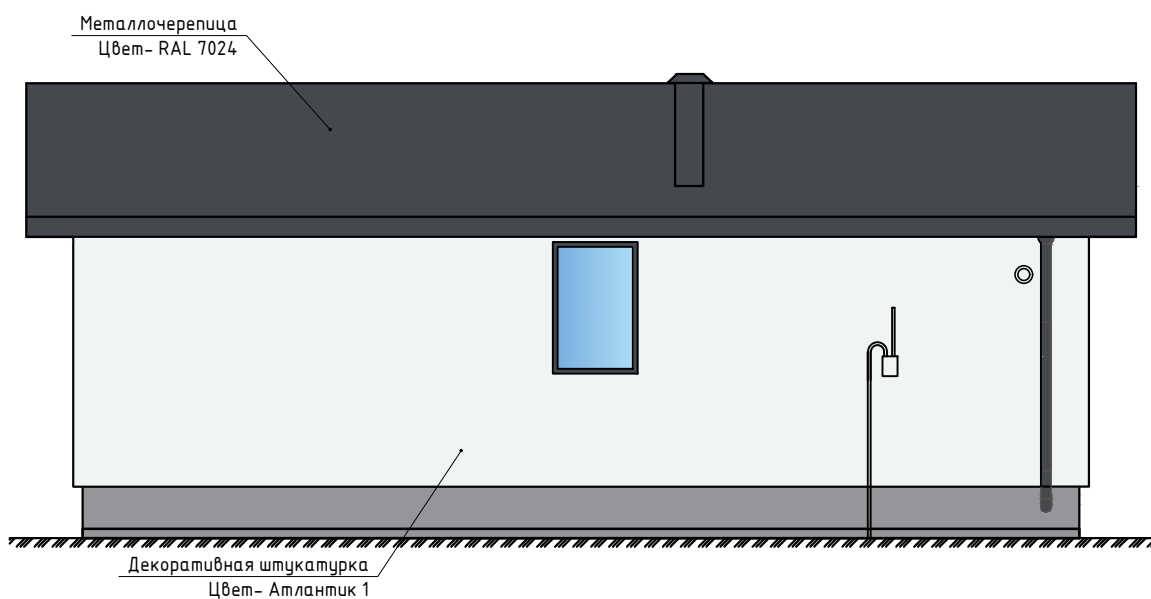

Количество и конфигурация секций в окнах показаны условно и уточняются на этапе согласования окон с производителем

Подпись и дата							АС				
	Изм.	Кол.уч.	Лист	№ док.	Подп.	Дата					
	Инж.-арх		Цветкова				одноэтажный дом площадью 60 кв.м.		Стадия	Лист	Листов
Инв. № подл.									П	10	28
							Архитектурно-строительные решения				

Разрез 1-1

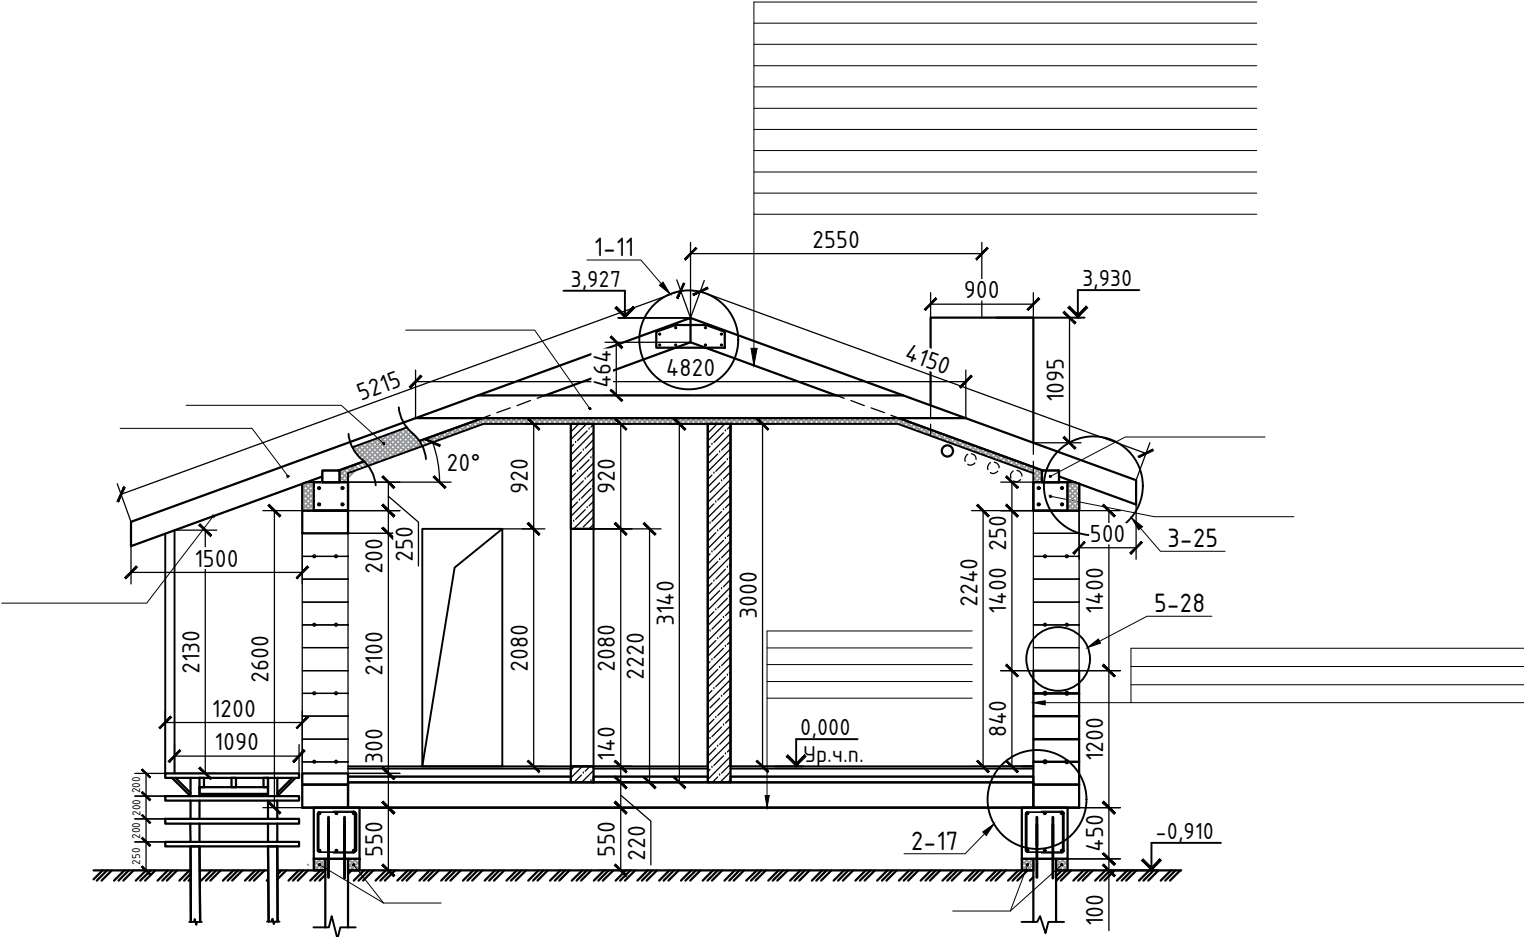

						АС			
Изм.	Кол.ч	Лист	№ док.	Подп.	Дата	одноэтажный дом площадью 60 кв.м.	Стадия	Лист	Листов
Инж.-арх	Цветкова						П	11	28
						Архитектурно-строительные решения			